| | | |
|---|---|---|
| AS OY RAUTA-KALEVA<br>PIEKSÄMÄKI | 1/50 | 29.12.1965 |
| VESI- JA VIEMÄRIJOHDOT<br>SALAOJAT<br>POHJAKERROS B-TALO | Pauro Palomäen<br>LAHTI puh. 23825<br>No 622 - 5 | B |

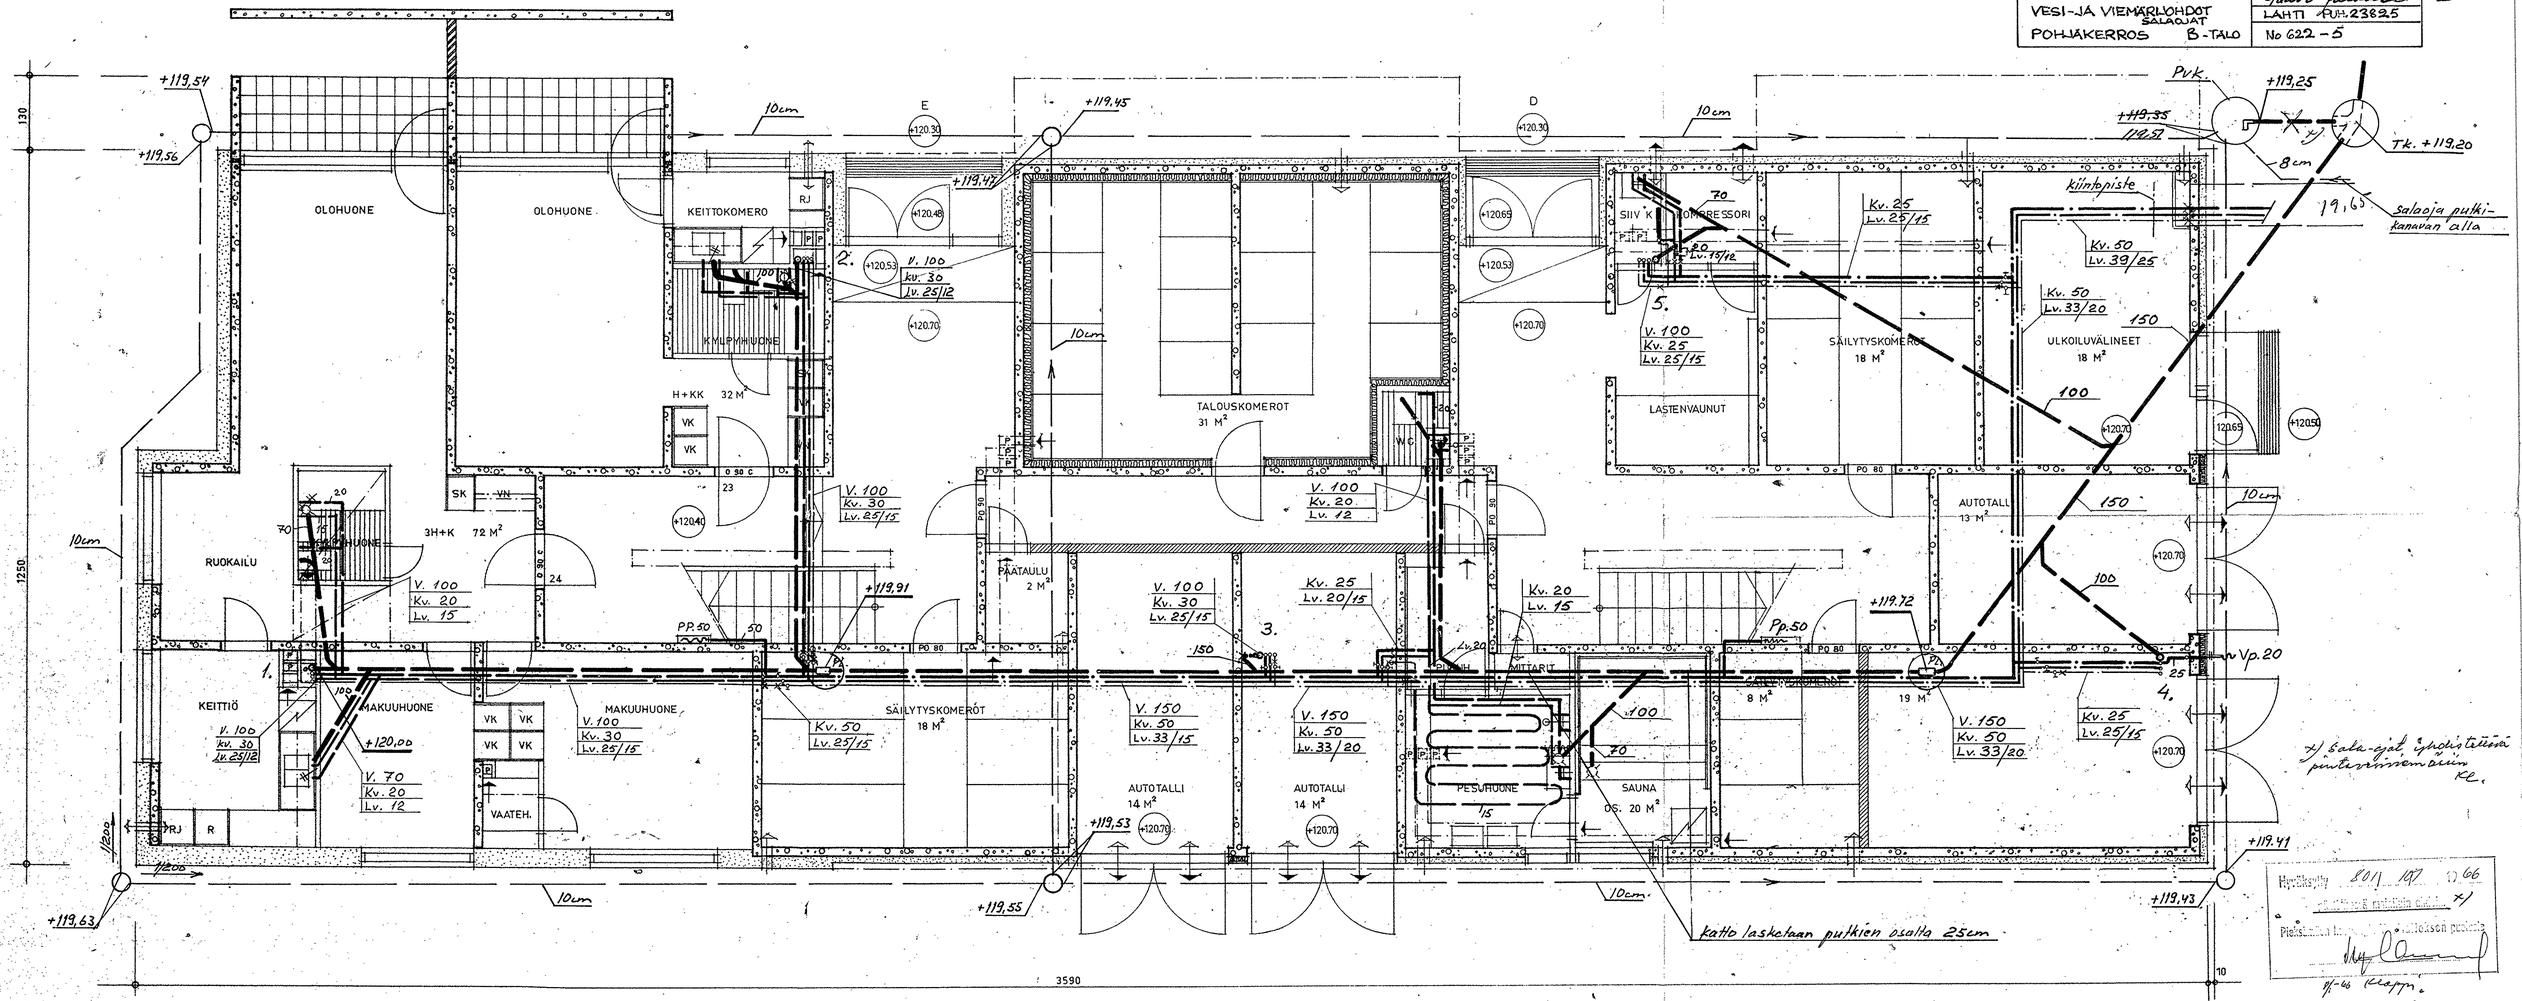


Hyväksytty 8/1 1967 17.66
Pieksämäen kaupungin vesilaitoksen puolesta

AS OY RAUTA KALEVA TALO B
POHJAKERROS 1 / 50
11. 12. -65