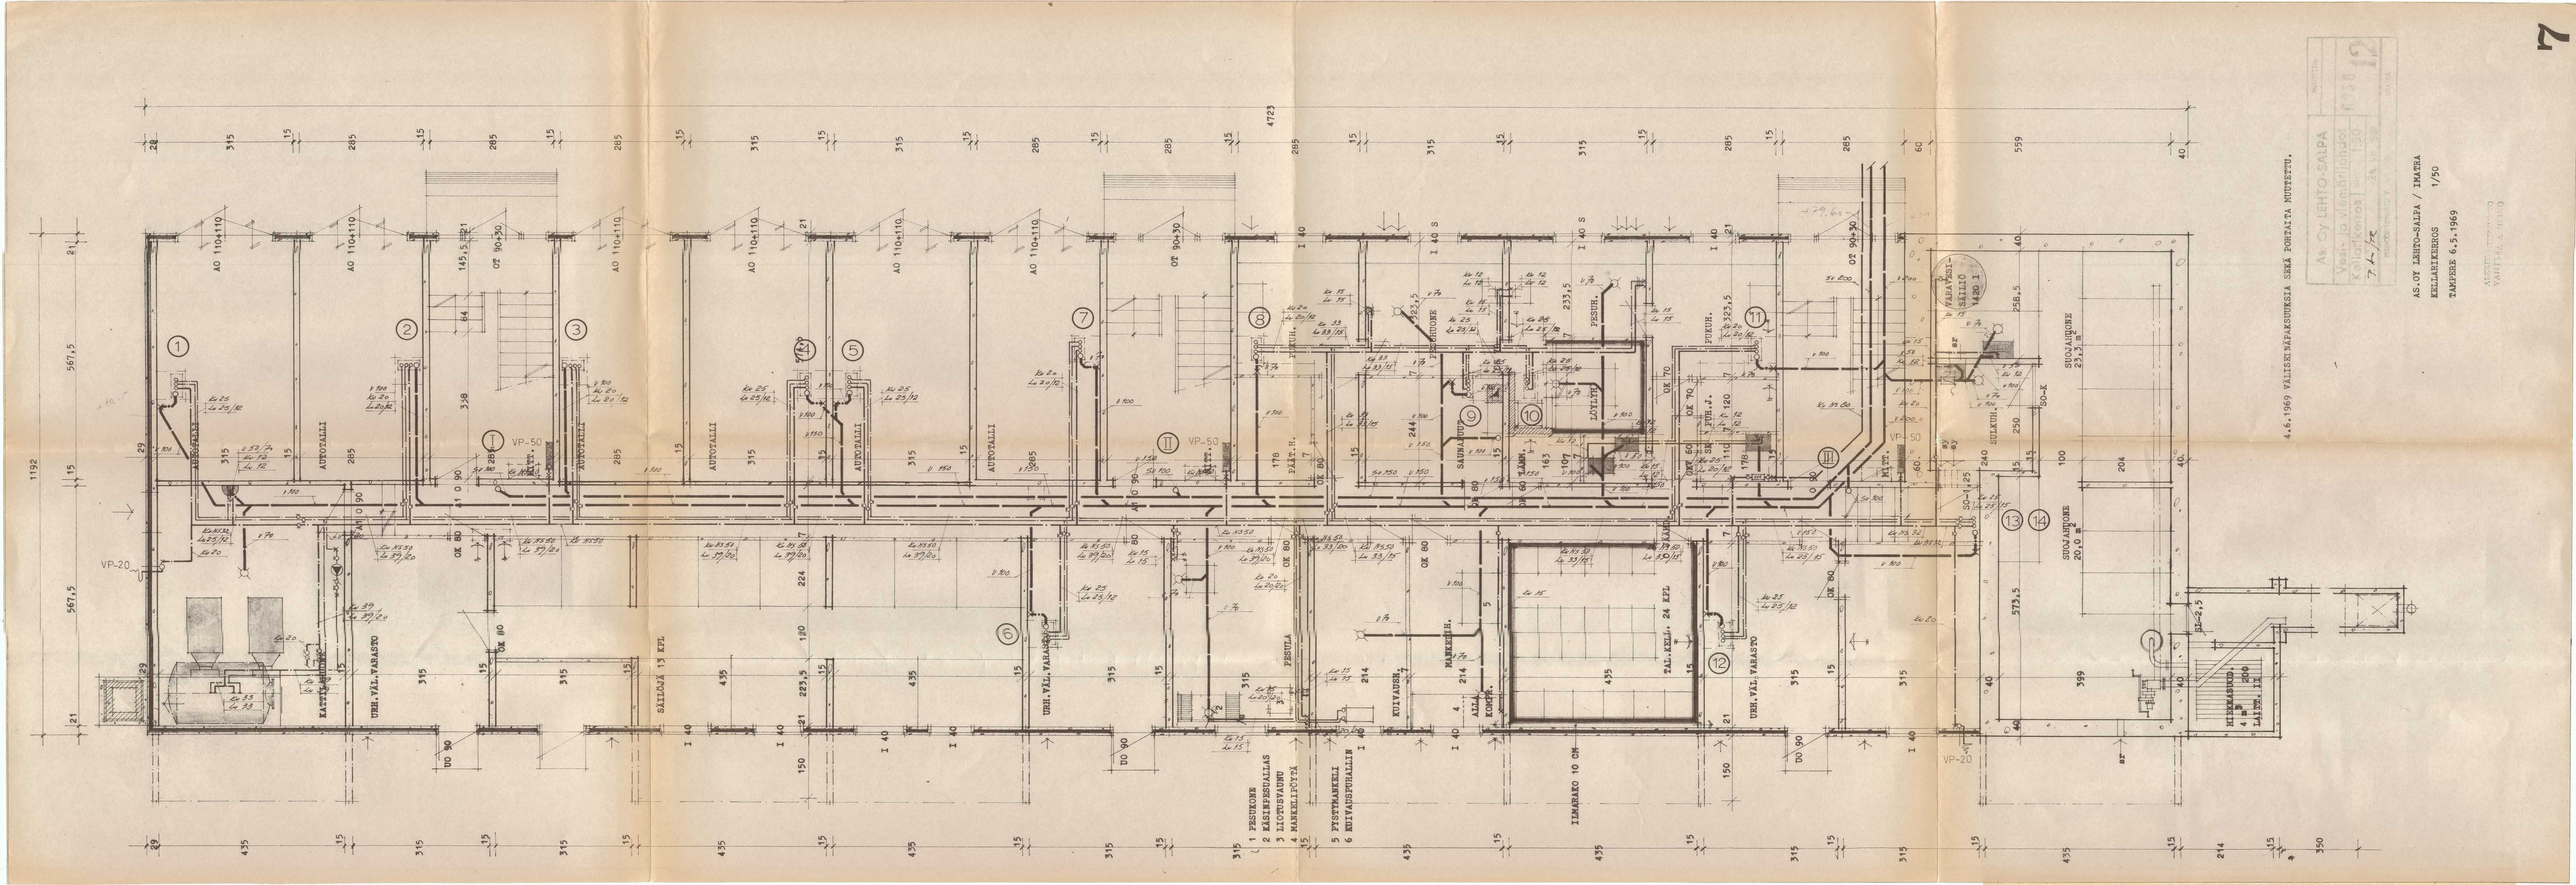
AS. OY LEHTO-SALPA / IMATRA
KELLARIKERROS 1/50
TAMPERE 6.5.1969
4.6.1969 VÄLISEKI RAPARSUUSSIA SEKÄ PORRASTA MUUTETTU.
As. Oy LEHTO-SALPA
Vesi- ja viemäriinjoh
Kellarikerros
1 PESUKONE
2 KÄSINPESUALLAS
3 LIOTUSVADMU
4 MANKELIPÖYTÄ
5 PYSYTMANKELI
6 KUIVADSPUHALIN
SÄILIÖJÄ 13 KPL
IMAMAKO 10 CM
PAL.KELL. 24 KPL
SAUNALAUT.
LOVIPUT.
PESUH.
KUIVADSH.
MANKELIH.
ALLA KOKER.
PESULA
KÄYTTÖHUONE
UREL.VÄL.VARASTO
AUTOPALLI
VP-50
VP-20
SIIVOUSHUONE 23,5 m²
SIIVOUSHUONE 20,0 m²
HISSIKASCO 4 m 200 LATIN. 12